


ARRANJO SOLAR - 2 STRINGS
2 STRINGS DE 8 PAINÉIS N-TOPCon Mono bifacial
MAX POTÊNCIA 9440 W, Voc 413,60 V, Isc 14,45 A
FABRICANTE: RONMA MODELO: RM-590W-182M/144TB 590 W

DIAGRAMA UNIFILAR

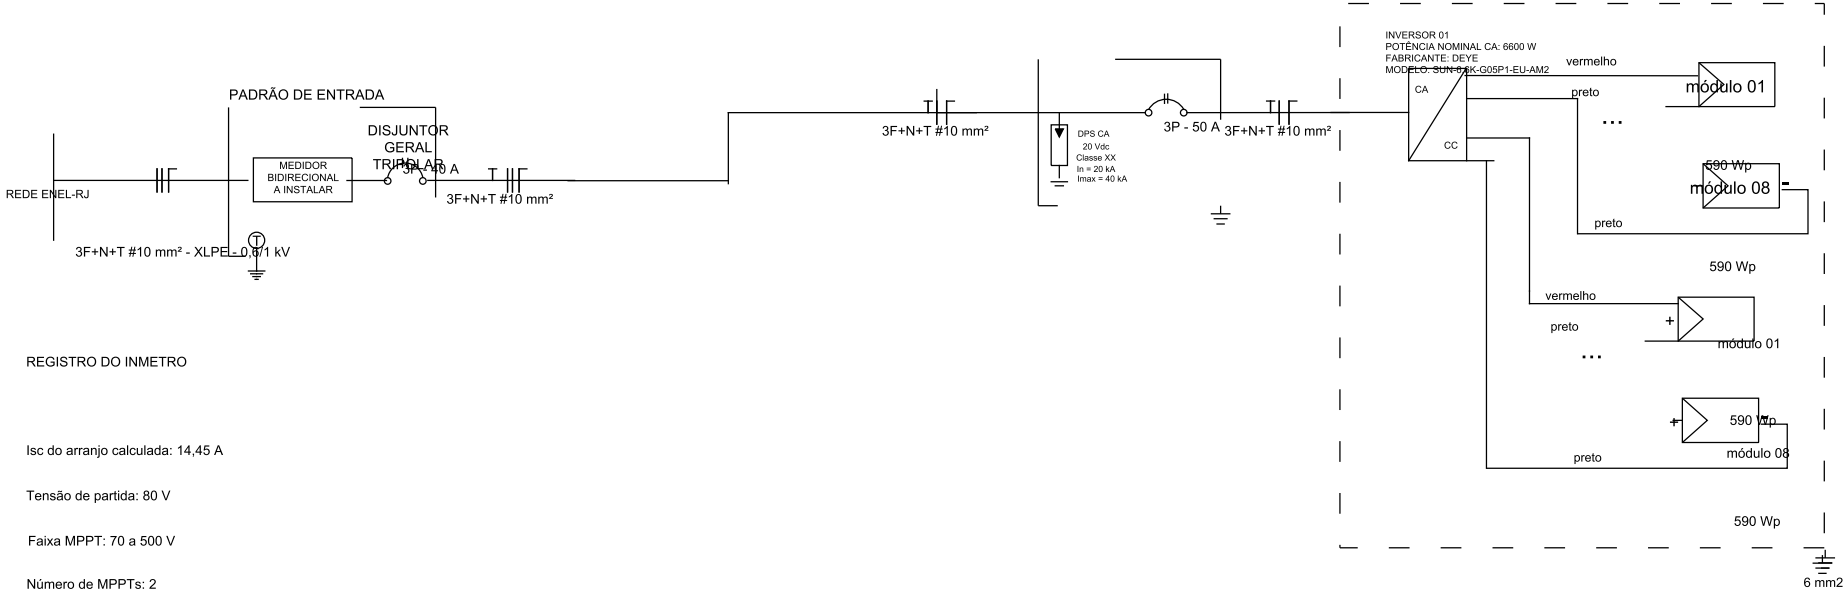

REGISTRO DO INMETRO

Isc do arranjo calculada: 14,45 A

Tensão de partida: 80 V

Faixa MPPT: 70 a 500 V

Número de MPPTs: 2

Máx. potência do gerador FV: 8,60 kWp

Potência máxima CA: 7260 VA

Tensão de conexão: 220 V Trifásico

Distorção harmônica total: 3 %

Fator de potência: 0,8 adiantado a 0,8 atrasado

Peso: 11 kg

Classe de proteção: Classe I

Topologia: Sem transformador


Temperatura ambiente: -25 a +60 °C

Conexões com o arranjo solar: 2 CC+ e CC-

Conexão com a rede: 3 polos CA + N + T

Bitola dos terminais CA: 10 mm²

DETALHE DAS PLACAS DE ADVERTÊNCIA A SEREM
INSTALADAS CONFORME Especificação Técnica 122

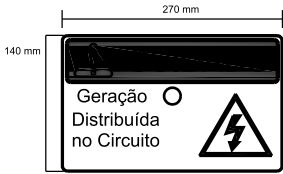

SITUAÇÃO DA UNIDADE CONSUMIDORA
(UTILIZAR VISUALIZAÇÃO VIA
MAPA OU SATELITE)

LOCALIZAÇÃO DA UC

Latitude: -22.8032807

Longitude: -43.3983188

Abrir no Google Maps:

google.com/maps?q=-22.80328

NOTAS OBRIGATÓRIAS

- O fornecedor dos inversores garante a desconexão da central geradora durante a manutenção do sistema da Concessionária ENEL;
- Quando da solicitação de vistoria deverá ser apresentado o Relatório de Comissionamento das Instalações de Conexão de acordo com os itens estabelecidos na ABNT NBR 16274, devidamente assinados pelo engenheiro/técnico responsável, indicando as características finais das instalações de conexão, os resultados dos ensaios e resultados dos testes e medições realizados;
- Os inversores deverão atender ao estabelecido na ABNT NBR IEC 62116 e Especificação Técnica 122 da ENEL.;
- O aterramento do sistema de geração deverá ser conectado ao sistema de aterramento da unidade consumidora;
- Os inversores deverão estar instalados em locais de fácil acesso, protegidos contra intempéries de acordo com o seu

suas características técnicas durante o processo de fiscalização/conexão da G.D;

- As instalações elétricas nestes locais deverão estar em conformidade com a NR-10, Normas técnicas/segurança da ENEL e ABNT;
- O projeto deverá atender todas as exigências da Especificação Técnica 122 - ENEL..

LEGENDA E ESPECIFICAÇÃO DOS EQUIPAMENTOS

	RM-590W-182M/144TB 590 W
	DISJUNTOR MONOPOLAR
	DISJUNTOR TRIPOLAR
	DPS CA
	DEYE - SUN-6.6K-G05P1-EU-AM2
	DPS CC
(ADICIONAR OUTROS ITENS SE NECESSÁRIO)	

RESERVADO A ENEL-RJ:

QUADRO DE REVISÕES:

REVISÃO Nº	DESCRIÇÃO	DATA
00	EMIÇÃO AUTOMÁTICA	
01	REVISÃO 1	XXXX/XXXX

PROJETO DE GERAÇÃO DISTRIBUÍDA (GD)

CIDADE DA OBRA: MARICÁ-RJ		SETOR DA OBRA: FOTOVOLTAICA	
ENDEREÇO DA OBRA: R 11 1046A QD 33 CASA 03 24914-140			
9,44 kWp		UNIDADE CONSUMIDORA 003121	
ASSINATURAS:			
PROPRIETÁRIO: WILSON FRANCISCO DOS SANTOS FILHO		CNPJ(CPF):	
AUTOR DO PROJETO:		CNPJ(CPF):	
ESPAÇO RESERVADO AO LOGO DA EMPRESA (SE HOUVER)	CONTEÚDO:	FRANCA:	
(LOGO)	01-DIAGRAMA UNIFILAR; 02-DETALHES;NOTAS; 03-SITUAÇÃO.	01 / 01	
	DESENHO: DIAGRAMA_WILSON_FRANCISCO DOS SANTOS		
	ESCALA: INDICADA		
ESTE PROJETO ESTÁ PROTEGIDO POR LEI DE DIREITO AUTURAL, SENDO PROIBIDA SUA REPRODUÇÃO TOTAL OU PARCIAL, SOB AS PENAS DA LEI 9.610 DE FEV/98			