


ARRANJO SOLAR - 2 STRINGS

2 STRINGS DE 5 PAINÉIS N-TOPCon Mono bifacial

MAX POTÊNCIA 5850 W, Voc 257,50 V, Isc 14,36 A

FABRICANTE: RONMA MODELO: RM-585W-182M/144TB 585 W

DIAGRAMA UNIFILAR

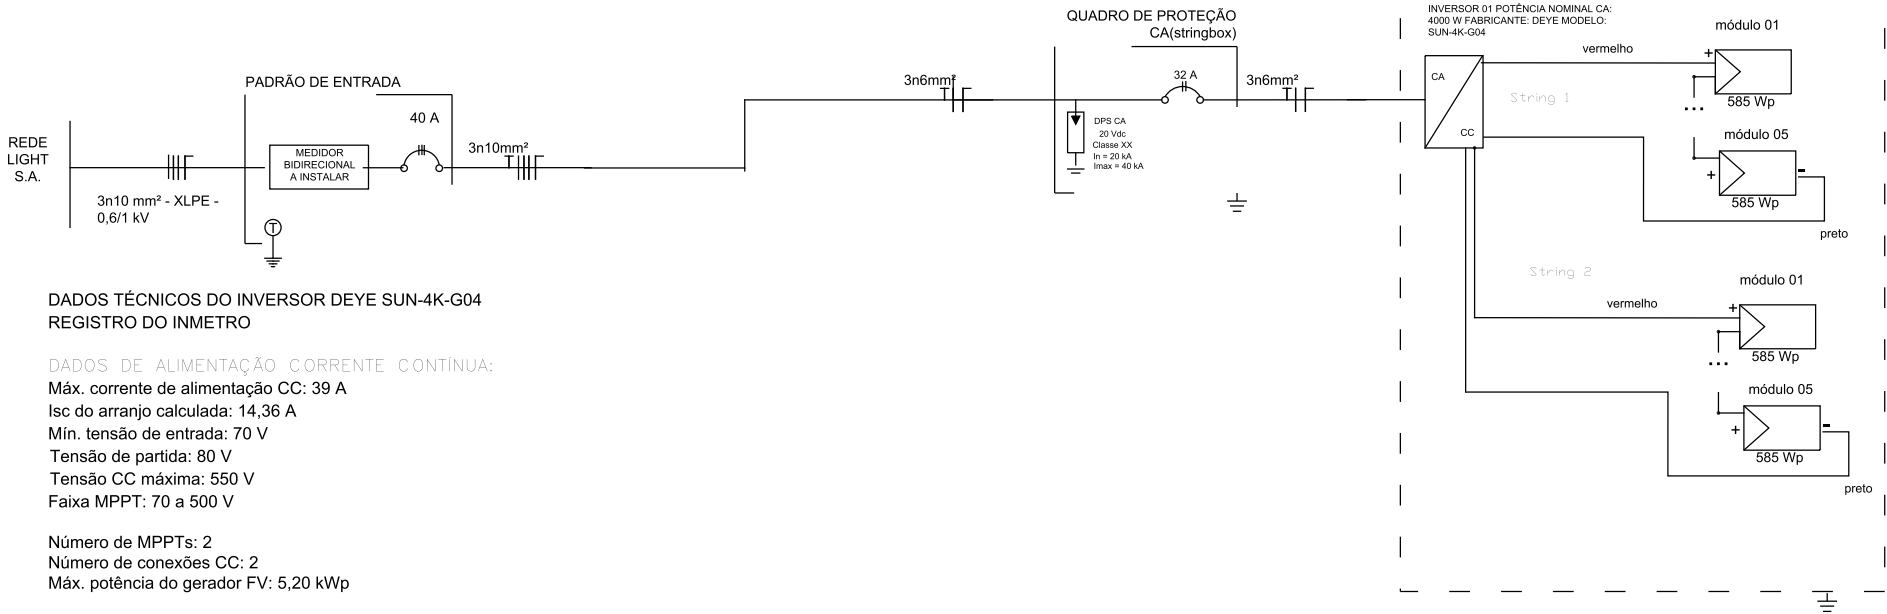

DADOS TÉCNICOS DO INVERSOR DEYE SUN-4K-G04

REGISTRO DO INMETRO

DADOS DE ALIMENTAÇÃO CORRENTE CONTINUA:

Máx. corrente de alimentação CC: 39 A

Isc do arranjo calculada: 14,36 A

Mín. tensão de entrada: 70 V

Tensão de partida: 80 V

Tensão CC máxima: 550 V

Faixa MPPT: 70 a 500 V

Número de MPPTs: 2

Número de conexões CC: 2

Máx. potência do gerador FV: 5,20 kWp

DADOS DE GERAÇÃO EM CORRENTE ALTERNADA:

Potência nominal CA: 4000 W

Potência máxima CA: 4400 VA

Corrente de saída nominal: 20 A

Tensão de conexão: 220 V Bifásico

Frequência: 60 Hz

Distorção harmônica total: 3 %

Fator de potência: 0,8 adiantado a 0,8 atrasado

DADOS GERAIS:

Dimensões: 330 x 310 x 172 mm

Peso: 11 kg

Grau de proteção: IP65

Classe de proteção: Classe I

Consumo noturno: < 1 W

Topologia: Sem transformador

Controle de temperatura: Refrigeração natural

Temperatura ambiente: -25 a +60 °C

Umidade relativa do ar: 0 a 100%

Conexões com o arranjo solar: 2 CC+ e CC-

Bitola dos terminais CC: 6 mm²

Conexão com a rede: 3 polos CA + T

Bitola dos terminais CA: 6 mm²


DETALHE DAS PLACAS DE ADVERTÊNCIA A SEREM

INSTALADAS CONFORME RECON-BT



PLACA DE ADVERTÊNCIA:

- 1) Material das placas: chapa galvanizada (43,5% zinco, 55% alumínio e 1,5% silício) nº 22 USG (0,79mm), cantos arredondados.
- 2) 2mm de espessura
- 3) Dimensões indicadas
- 4) Pintura de Fundo: Epóxi.
- 5) Pintura das letras: tinta eletrostática em pó.
- 6) Na chapa deverá ser aplicada uma demão de fundo anti-corrosivo de espessura mínima de 30µm (frente e fundo).

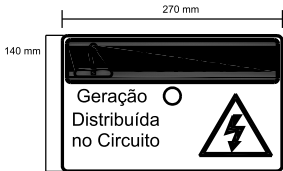

Deve ser instalada uma placa de advertência no poste onde se encontra o transformador de distribuição que alimenta o circuito de baixa tensão da unidade consumidora com geração distribuída, com os seguintes dizeres: "CUIDADO - GERAÇÃO DISTRIBUÍDA NO CIRCUITO". Quando solicitado pela LIGHT, o acessante deve fornecer a placa. A placa de advertência deve ser confeccionada conforme Figura 3 e possuir as seguintes características:

- material: chapa de fibra de vidro altamente resistente as intempéries e corrosão, cantos arredondados;
- dimensões da placa: 140 x 270 mm;
- cor do fundo: amarela, em epóxi;
- letras: cor preta, tinta eletrostática em pó;

NOTAS OBRIGATÓRIAS

- O fornecedor dos inversores garante a desconexão da central geradora durante a manutenção do sistema da Concessionária LIGHT;
- Quando da solicitação de vistoria deverá ser apresentado o Relatório de Comissionamento das Instalações de Conexão de acordo com os itens estabelecidos na ABNT NBR 16274, devidamente assinados pelo engenheiro/técnico responsável, indicando as características finais das instalações de conexão, os resultados dos ensaios e resultados dos testes e medições realizados;
- Os inversores deverão atender ao estabelecido na ABNT NBR IEC 62116 e RECON-BT - LIGHT;
- O aterramento do sistema de geração deverá ser conectado ao sistema de aterramento da unidade consumidora;
- Os inversores deverão estar instalados em locais de fácil acesso, protegidos contra intempéries de acordo com o seu grau de proteção (IP), que permitam facilmente a verificação de suas características técnicas durante o processo de fiscalização/conexão da G.D;
- As instalações elétricas nestes locais deverão estar em conformidade com a NR-10, Normas técnicas/segurança da LIGHT e ABNT;
- O projeto deverá atender todas as exigências da RECON-BT - LIGHT.

LEGENDA E ESPECIFICAÇÃO DOS EQUIPAMENTOS

|                                        |                                            |
|----------------------------------------|--------------------------------------------|
|                                        | PLACA SOLAR RONMA RM-585W-182M/144TB 585 W |
|                                        | DISJUNTOR MONOPOLAR                        |
|                                        | DISJUNTOR TRIPOLAR                         |
|                                        | DPS CA                                     |
|                                        | INVERSOR DE POTENCIA DEYE - SUN-4K-G04     |
|                                        | DPS CC                                     |
| (ADICIONAR OUTROS ITENS SE NECESSÁRIO) |                                            |

RESERVADO A LIGHT:

QUADRO DE REVISÕES:

| REVISÃO Nº | DESCRIÇÃO          | DATA       |
|------------|--------------------|------------|
| 02         | EMISSÃO AUTOMÁTICA |            |
| 01         | REVISÃO 1          | 04/06/2024 |
|            |                    |            |
|            |                    |            |

PROJETO DE GERAÇÃO DISTRIBUÍDA (GD)

(MICROGERAÇÃO - POTÊNCIA MENOR OU IGUAL A 10kW)

|                                                                                                 |  |                                            |  |
|-------------------------------------------------------------------------------------------------|--|--------------------------------------------|--|
| LOCAL DO BOMBA: SAO JOAO DE MERITI, RJ                                                          |  | NOME DA UNIDADE CONSUMIDORA                |  |
| ENDEREÇO DA OBRA: R JOSE DOS REIS 47 LJ COELHO DA ROCHA I SAO JOAO DE MERITI, RJ, CEP 25550-780 |  |                                            |  |
| POTÊNCIA: 5,85 kWp                                                                              |  | UNIDADE CONSUMIDORA (Nº): 2.783.802.059-28 |  |
| CONDIÇÕES                                                                                       |  |                                            |  |
| ASSINATURA DO PROJETISTA: SONIA MERELLES ALMEIDA                                                |  | ASSINATURA DO CLIENTE:                     |  |
| ASSINATURA DO PROJETISTA: SONIA MERELLES ALMEIDA                                                |  | ASSINATURA DO CLIENTE:                     |  |
| LOCAL DO BOMBA: SAO JOAO DE MERITI, RJ                                                          |  | NOME DA UNIDADE CONSUMIDORA                |  |
| ENDEREÇO DA OBRA: R JOSE DOS REIS 47 LJ COELHO DA ROCHA I SAO JOAO DE MERITI, RJ, CEP 25550-780 |  | POTÊNCIA: 5,85 kWp                         |  |
| UNIDADE CONSUMIDORA (Nº): 2.783.802.059-28                                                      |  | CONDIÇÕES                                  |  |
| ASSINATURA DO PROJETISTA: SONIA MERELLES ALMEIDA                                                |  | ASSINATURA DO CLIENTE:                     |  |
| ASSINATURA DO PROJETISTA: SONIA MERELLES ALMEIDA                                                |  |                                            |  |