


ARRANJO SOLAR EM SÉRIE  
10 PAINÉIS N-TOPCon Mono bifacial  
MAX POTÊNCIA 5850 W, Voc 257,50 V, Isc 14,36 A  
FABRICANTE: RONMA MODELO: RM-585W-182M/144TB 585 W

## DIAGRAMA UNIFILAR

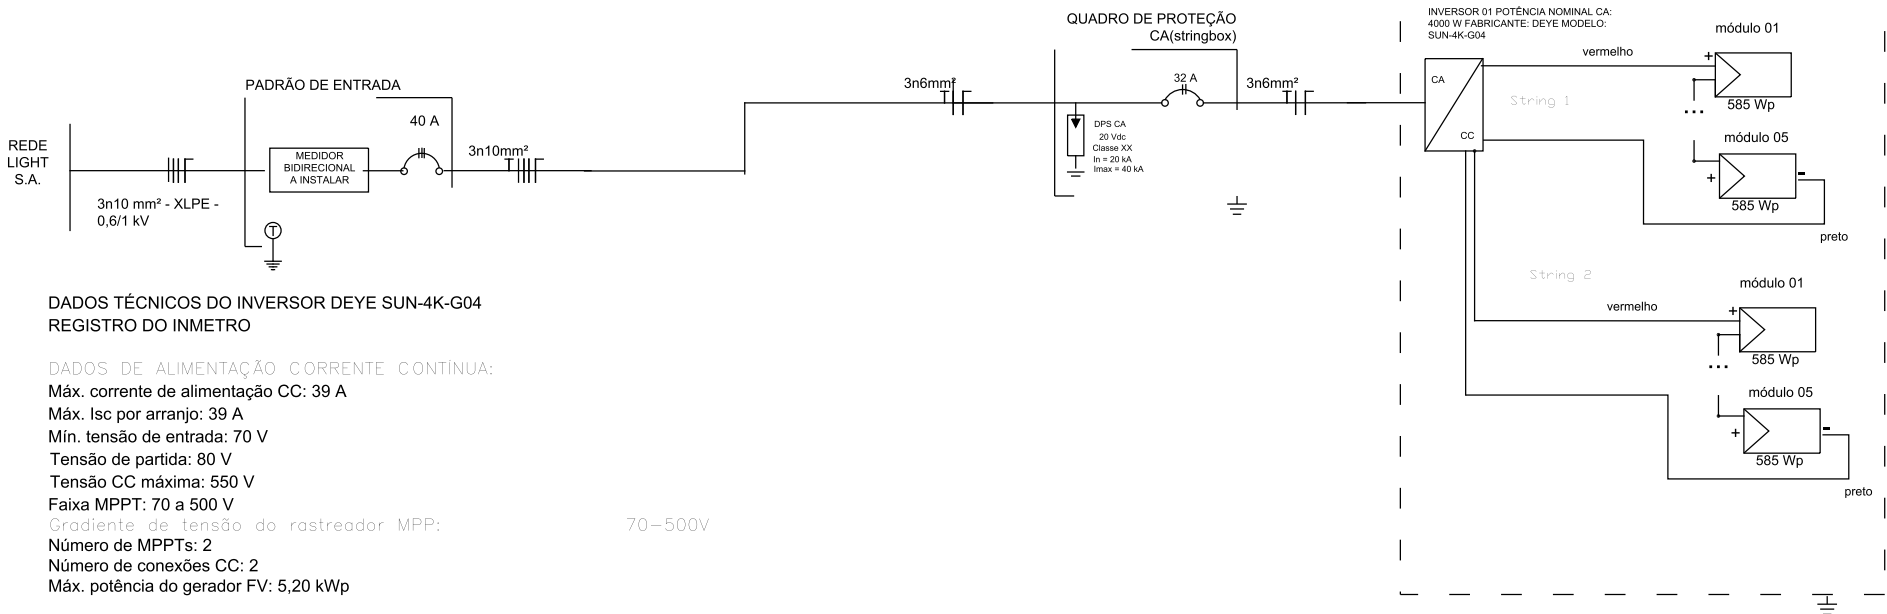

### DADOS TÉCNICOS DO INVERSOR DEYE SUN-4K-G04 REGISTRO DO INMETRO

#### DADOS DE ALIMENTAÇÃO CORRENTE CONTÍNUA:

Máx. corrente de alimentação CC: 39 A  
Máx. Isc por arranjo: 39 A  
Mín. tensão de entrada: 70 V  
Tensão de partida: 80 V  
Tensão CC máxima: 550 V  
Faixa MPPT: 70 a 500 V  
Gradiente de tensão do rastreador MPP: 70–500V  
Número de MPPTs: 2  
Número de conexões CC: 2  
Máx. potência do gerador FV: 5,20 kWp

#### DADOS DE GERAÇÃO EM CORRENTE ALTERNADA:

Potência nominal CA: 4000 W  
Potência máxima CA: 4400 VA  
Corrente de saída nominal: 20 A  
Tensão de conexão: 220 V Bifásico  
Frequência: 60 Hz  
Distorção harmônica total: 3 %  
Fator de potência: 0,8 adiantado a 0,8 atrasado

#### DADOS GERAIS:

Dimensões: 330 x 310 x 172 mm  
Peso: 11 kg  
Grau de proteção: IP65  
Classe de proteção: Classe I  
Consumo noturno: < 1 W  
Topologia: Sem transformador  
Controle de temperatura: Refrigeração natural  
Temperatura ambiente: -25 a +60 °C  
Umidade relativa do ar: 0 a 100%  
Conexões com o arranjo solar: 2 CC+ e CC-  
Bitola dos terminais CC: 6 mm²  
Conexão com a rede: 3 polos CA + T  
Bitola dos terminais CA: 6 mm²

### DETALHE DAS PLACAS DE ADVERTÊNCIA A SEREM INSTALADAS CONFORME RECON-BT



#### PLACA DE ADVERTÊNCIA:

- Material das placas: chapa galvanizada (43,5% zinco, 55% alumínio e 1,5% silício) nº 22 USG (0,79mm), cantos arredondados.
- 2mm de espessura
- Dimensões indicadas
- Pintura de Fundo: Epóxi.
- Pintura das letras: tinta eletrostática em pó.
- Na chapa deverá ser aplicada uma demão de fundo anti-corrosivo de espessura mínima de 30µm (frente e fundo).



Deve ser instalada uma placa de advertência no poste onde se encontra o transformador de distribuição que alimenta o circuito de baixa tensão da unidade consumidora com geração distribuída, com os seguintes dizeres: "CUIDADO - GERAÇÃO DISTRIBUÍDA NO CIRCUITO". Quando solicitado pela LIGHT, o acessante deve fornecer a placa. A placa de advertência deve ser confeccionada conforme Figura 3 e possuir as seguintes características:

- material: chapa de fibra de vidro altamente resistente as intempéries e corrosão, cantos arredondados;
- dimensões da placa: 140 x 270 mm;
- cor do fundo: amarela, em epóxi;
- letras: cor preta, tinta eletrostática em pó;

## NOTAS OBRIGATÓRIAS

- O fornecedor dos inversores garante a desconexão da central geradora durante a manutenção do sistema da Concessionária LIGHT;
- Quando da solicitação de vistoria deverá ser apresentado o Relatório de Comissionamento das Instalações de Conexão de acordo com os itens estabelecidos na ABNT NBR 16274, devidamente assinados pelo engenheiro/técnico responsável, indicando as características finais das instalações de conexão, os resultados dos ensaios e resultados dos testes e medições realizados;
- Os inversores deverão atender ao estabelecido na ABNT NBR IEC 62116 e RECON-BT - LIGHT;
- O aterramento do sistema de geração deverá ser conectado ao sistema de aterramento da unidade consumidora;
- Os inversores deverão estar instalados em locais de fácil acesso, protegidos contra intempéries de acordo com o seu grau de proteção (IP), que permitam facilmente a verificação de suas características técnicas durante o processo de fiscalização/conexão da G.D;
- As instalações elétricas nestes locais deverão estar em conformidade com a NR-10, Normas técnicas/segurança da LIGHT e ABNT;
- O projeto deverá atender todas as exigências da RECON-BT - LIGHT.

### LEGENDA E ESPECIFICAÇÃO DOS EQUIPAMENTOS

|                                        |                                            |
|----------------------------------------|--------------------------------------------|
|                                        | PLACA SOLAR RONMA RM-585W-182M/144TB 585 W |
|                                        | DISJUNTOR MONOPOLAR                        |
|                                        | DISJUNTOR TRIPOLAR                         |
|                                        | DPS CA                                     |
|                                        | INVERSOR DE POTENCIA DEYE - SUN-4K-G04     |
|                                        | DPS CC                                     |
| (ADICIONAR OUTROS ITENS SE NECESSÁRIO) |                                            |

RESERVADO A LIGHT:

### QUADRO DE REVISÕES:

| REVISÃO Nº | DESCRIÇÃO          | DATA       |
|------------|--------------------|------------|
| 02         | EMISSÃO AUTOMÁTICA |            |
| 01         | REVISÃO 1          | 04/06/2024 |
|            |                    |            |
|            |                    |            |

## PROJETO DE GERAÇÃO DISTRIBUÍDA (GD) (MICROGERAÇÃO - POTÊNCIA MENOR OU IGUAL A 10kW)

|   |  |                                                                        |  |
|---|--|------------------------------------------------------------------------|--|
| UNIDADE DE ORIGEM: SAO JOAO DE MERITI, RJ   |  | NOME DA UNIDADE POTENCIÁVEL:                                           |  |
| ENDEREÇO DA OBRA: R JOSE DOS REIS 47 LJ COELHO DA ROCHA I SAO JOAO DE MERITI, RJ, CEP 25550-780                                                   |  |                                                                        |  |
| POTÊNCIA: 5,85 kWp   |  | UNIDADE CONSUMIDORA (N°): 2.783.802.059-28                             |  |
| CONDICIONAMENTO:   |  |                                                                        |  |
| AUTOR DO PROJETO: SONIA MERELLES ALMEIDA   |  | CONDIÇÃO:                                                              |  |
| AUTOR DO PROJETO:   |  | CONDIÇÃO:                                                              |  |
| UNIDADE DE ORIGEM DO FOLIO DE PLANILHAS DO PROJETO:                                                                                               |  | PROJETO: 01-DIAGRAMA UNIFILAR;<br>02- DETALHES/NOTAS;<br>03- SITUAÇÃO; |  |
| (LOGO)   |  | REVISÃO: 01/01                                                         |  |
|   |  | PROJETO: DIAGRAMA, SONIA, MERELLES, ALMEIDA                            |  |
|   |  | PROJETO: INDICAÇÃO                                                     |  |
| ESTE PROJETO É UM PRODUTO DA LIGHT E SUJEITO A ATUALIZAÇÃO. NÃO PERMITA SUA REPRODUÇÃO TOTAL OU PARCIAL, SOB AS PENAS DA LEI DE DIREITO DE AUTOR. |  |                                                                        |  |