


ARRANJO SOLAR EM SÉRIE
8 PAINÉIS N-TOPCon Mono bifacial
MAX POTÊNCIA 4680 W,Voc 412 V, Isc 14,36 A
FABRICANTE: RONMA MODELO: RM-585W-182M/144TB 585 W

DIAGRAMA UNIFILAR

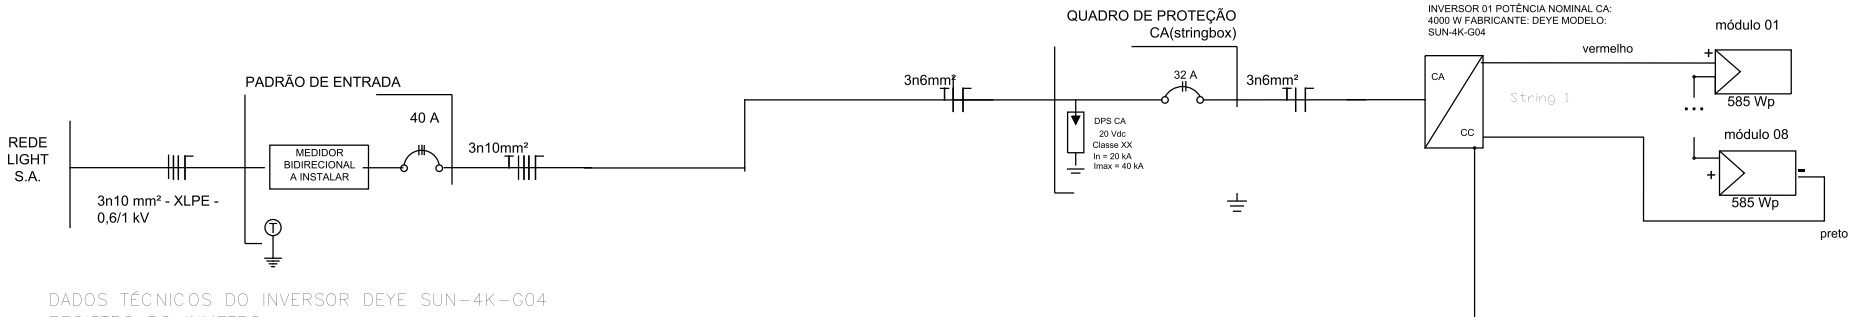

DADOS TÉCNICOS DO INVERSOR DEYE SUN-4K-G04
REGISTRO DO INMETRO

DADOS DE ALIMENTAÇÃO CORRENTE CONTÍNUA:
Máx. corrente de alimentação CC: 39 A
Máx. Isc por arranjo: 39 A
Mín. tensão de entrada: 70 V
Tensão de partida: 80 V
Tensão CC máxima: 550 V
Faixa MPPT: 70 a 500 V
Gradiente de tensão do rastreador MPP: 70-500V
Número de MPPTs: 2
Número de conexões CC: 2
Máx. potência do gerador FV: 5,20 kWp

DADOS DE GERAÇÃO EM CORRENTE ALTEERNADA:
Potência nominal CA: 4000 W
Potência máxima CA: 4400 VA
Corrente de saída nominal: 20 A
Tensão de conexão: 220 V Bifásico
Frequência: 60 Hz
Distorção harmônica total: 3 %
Fator de potência: 0,8 adiantado a 0,8 atrasado


DADOS GERAIS:
Dimensões: 330 x 310 x 172 mm
Peso: 11 kg
Grau de proteção: IP65
Classe de proteção: Classe I
Consumo noturno: < 1 W
Topologia: Sem transformador
Controle de temperatura: Refrigeração natural
Temperatura ambiente: -25 a +60 °C
Umidade relativa do ar: 0 a 100%
Conexões com o arranjo solar: 2 CC+ e CC-
Bitola dos terminais CC: 6 mm²
Conexão com a rede: 3 polos CA + T
Bitola dos terminais CA: 6 mm²

DETALHE DAS PLACAS DE ADVERTÊNCIA A SEREM
INSTALADAS CONFORME RECON-BT



PLACA DE ADVERTÊNCIA:

- 1) Material das placas: chapa galvanizada (43,5% zinco, 55% alumínio e 1,5% silício) nº 22 USG (0,79mm), cantos arredondados.
- 2) 2mm de espessura
- 3) Dimensões indicadas
- 4) Pintura de Fundo: Epóxi.
- 5) Pintura das letras: tinta eletrostática em pó.
- 6) Na chapa deverá ser aplicada uma demão de fundo anti-corrosivo de espessura mínima de 30µm (frente e fundo).

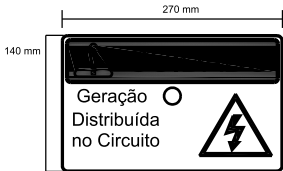

Deve ser instalada uma placa de advertência no poste onde se encontra o transformador de distribuição que alimenta o circuito de baixa tensão da unidade consumidora com geração distribuída, com os seguintes dizeres: "CUIDADO - GERAÇÃO DISTRIBUÍDA NO CIRCUITO". Quando solicitado pela LIGHT, o acessante deve fornecer a placa. A placa de advertência deve ser confeccionada conforme Figura 3 e possuir as seguintes características:

- material: chapa de fibra de vidro altamente resistente as intempéries e corrosão, cantos arredondados;
- dimensões da placa: 140 x 270 mm;
- cor do fundo: amarela, em epóxi;
- letras: cor preta, tinta eletrostática em pó;

NOTAS OBRIGATÓRIAS

- O fornecedor dos inversores garante a desconexão da central geradora durante a manutenção do sistema da Concessionária LIGHT;
- Quando da solicitação de vistoria deverá ser apresentado o Relatório de Comissionamento das Instalações de Conexão de acordo com os itens estabelecidos na ABNT NBR 16274, devidamente assinados pelo engenheiro/técnico responsável, indicando as características finais das instalações de conexão, os resultados dos ensaios e resultados dos testes e medições realizados;
- Os inversores deverão atender ao estabelecido na ABNT NBR IEC 62116 e RECON-BT - LIGHT;
- O aterramento do sistema de geração deverá ser conectado ao sistema de aterramento da unidade consumidora;
- Os inversores deverão estar instalados em locais de fácil acesso, protegidos contra intempéries de acordo com o seu grau de proteção (IP), que permitam facilmente a verificação de suas características técnicas durante o processo de fiscalização/conexão da G.D;
- As instalações elétricas nestes locais deverão estar em conformidade com a NR-10, Normas técnicas/segurança da LIGHT e ABNT;
- O projeto deverá atender todas as exigências da RECON-BT - LIGHT.

LEGENDA E ESPECIFICAÇÃO DOS EQUIPAMENTOS

- PLACA SOLAR RONMA RM-585W-182M/144TB 585 W
- DISJUNTOR MONOPOLAR
- DISJUNTOR TRIPOLAR
- DPS CA
- INVERSOR DE POTENCIA DEYE - SUN-4K-G04
- DPS CC
- (ADICIONAR OUTROS ITENS SE NECESSÁRIO)

RESERVADO A LIGHT:

QUADRO DE REVISÕES:

REVISÃO Nº	DESCRIÇÃO	DATA
00	VERSÃO AUTOMÁTICA	
01	REVISÃO 1	04/06/2024

PROJETO DE GERAÇÃO DISTRIBUÍDA (GD)
(MICROGERAÇÃO - POTÊNCIA MENOR OU IGUAL A 10kW)

UNIDADE DE BARRA: SAO JOAO DE MERITI, RJ		NOME DA UNIDADE FOTOVOLTAICA: SAO JOAO DE MERITI, RJ	
ENDEREÇO DA UNIDADE: R JOSE DOS REIS 47 LJ COELHO DA ROCHA / SAO JOAO DE MERITI, RJ, CEP 25550-780			
POTÊNCIA: 4,68 kWp		UNIDADE CONSUMIDORA (N°): 2.783.802.059-28	
CONDICIONAMENTO:			
PROFESSOR(A): SONIA MEIRELLES ALMEIDA		DISCIPLINA: PF	
AUTOR DO PROJETO:		ORIENTADOR(A):	
TÍTULO DO PROJETO: PROJETO DE GERAÇÃO DISTRIBUÍDA (GD)		NÚMERO DO PROJETO: 01/01	
(LOGO)		01/01	
ESTE PROJETO É UM PROJETO DE BOMBA D'ÁGUA, NÃO DEVE SER REPRODUZIDO TOTAL OU PARCIALMENTE, SOB AS PENAS DA LEI DE DIREITO DE AUTOR.			