


2 STRINGS DE 7 PAINÉIS FOTOVOLTAICOS
14 PAINÉIS MONOCRISTALINOS 144 CELULAS
MAX POTÊNCIA 8190W, Voc 721 V, Isc 14.36 A
FABRICANTE: RONMA SOLAR MODELO: RM-585W-182M-144TB 585 W

DIAGRAMA UNIFILAR

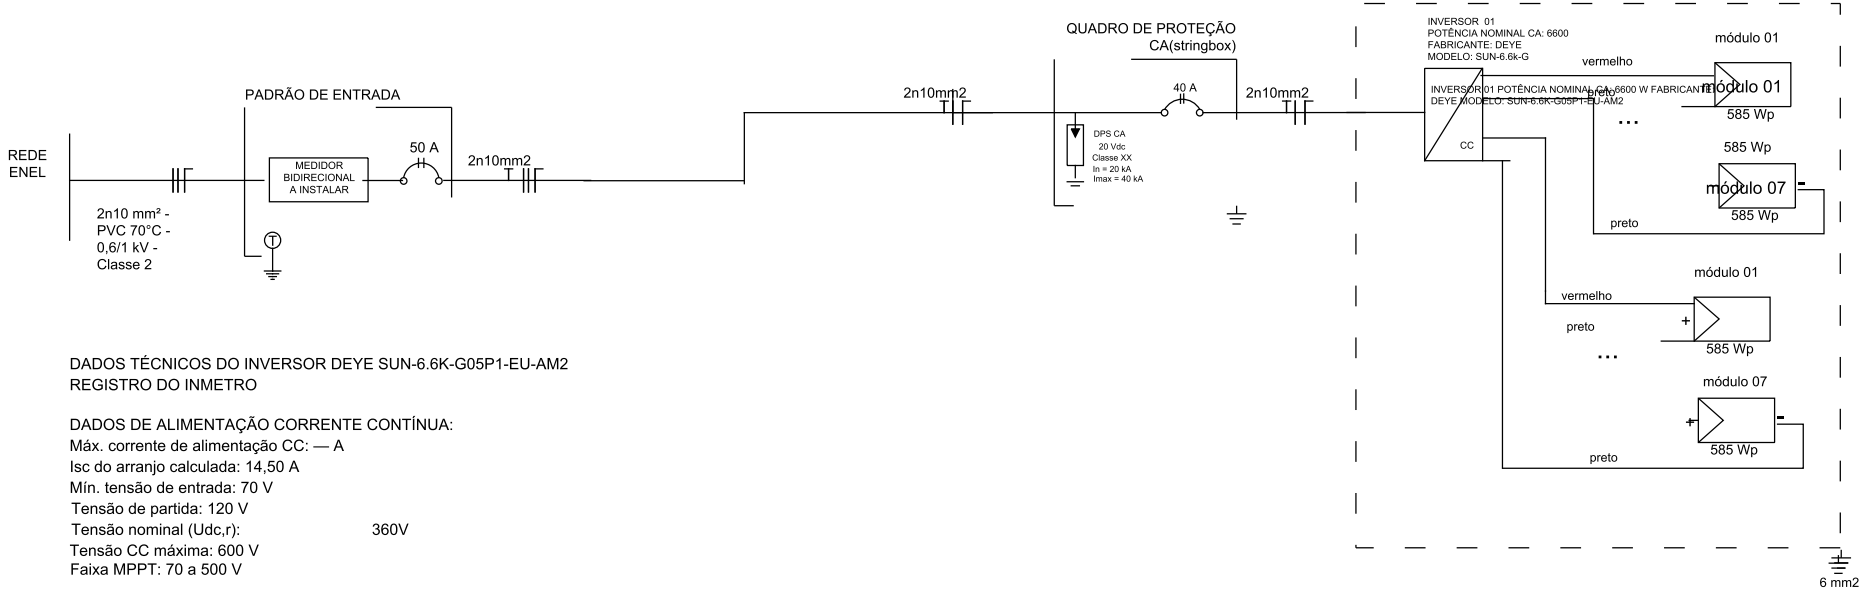

DADOS TÉCNICOS DO INVERSOR DEYE SUN-6.6K-G05P1-EU-AM2
REGISTRO DO INMETRO

DADOS DE ALIMENTAÇÃO CORRENTE CONTÍNUA:
Máx. corrente de alimentação CC: — A
Isc do arranjo calculada: 14,50 A
Mín. tensão de entrada: 70 V
Tensão de partida: 120 V
Tensão nominal (Udc,r): 360V
Tensão CC máxima: 600 V
Faixa MPPT: 70 a 500 V

Número de MPPTs: 2
Número de conexões CC: —

DADOS DE GERAÇÃO EM CORRENTE ALTEERNADA:
Potência Nominal CA: 6600W
Potência nominal CA: 6600 W
Potência máxima CA: 0 VA
Tensão de conexão com a rede: 220V Monofásico
Tensão de conexão: 220 V Bifásico
Distorção Harmônica Total: < 3 %
Distorção harmônica total: ≤ 3 %


Fator de potência:
Dimensões (altura x largura x prof.): 300 x 310 x 172mm
Peso: 11 kg
Dimensões: 330 x 310 x 172 mm
Peso: 11 kg
Grau de proteção: IP65
Classe de proteção: Classe I
Consumo noturno: < 1 W
Topologia: Sem transformador
Controle de temperatura: Refrigeração natural
Conexões com o arranjo solar 4x CC+ e 4x CC-
Umidade relativa do ar: 0 a 100%
Conexão com a Rede: 3 polos CA FN+T
Bitola dos terminais CC: 6 mm²

DETALHE DAS PLACAS DE ADVERTÊNCIA A SEREM
INSTALADAS CONFORME Especificação Técnica 122



PLACA DE ADVERTÊNCIA:

- 1) Material das placas: chapa galvanizada (43,5% zinco, 55% alumínio e 1,5% silício) nº 22 USG (0,79mm), cantos arredondados.
- 2) 2mm de espessura
- 3) Dimensões indicadas
- 4) Pintura de Fundo: Epóxi.
- 5) Pintura das letras: tinta eletrostática em pó.
- 6) Na chapa deverá ser aplicada uma demão de fundo anti-corrosivo de espessura mínima de 30µm (frente e fundo).

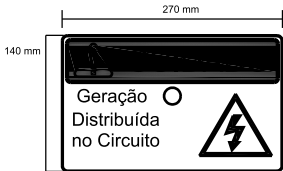


Deve ser instalada uma placa de advertência no poste onde se encontra o transformador de distribuição que alimenta o circuito de baixa tensão da unidade consumidora com geração distribuída, com os seguintes dizeres: "CUIDADO - GERAÇÃO DISTRIBUÍDA NO CIRCUITO". Quando solicitado pela ENEL, o acessante deve fornecer a placa. A placa de advertência deve ser confeccionada conforme Figura 3 e possuir as seguintes características:

- material: chapa de fibra de vidro altamente resistente as intempéries e corrosão, cantos arredondados;
- dimensões da placa: 140 x 270 mm;
- cor do fundo: amarela, em epóxi;
- letras: cor preta, tinta eletrostática em pó;

NOTAS OBRIGATÓRIAS

- O fornecedor dos inversores garante a desconexão da central geradora durante a manutenção do sistema da Concessionária ENEL;
- Quando da solicitação de vistoria deverá ser apresentado o Relatório de Comissionamento das Instalações de Conexão de acordo com os itens estabelecidos na ABNT NBR 16274, devidamente assinados pelo engenheiro/técnico responsável, indicando as características finais das instalações de conexão, os resultados dos ensaios e resultados dos testes e medições realizados;
- Os inversores deverão atender ao estabelecido na ABNT NBR IEC 62116 e Especificação Técnica 122 da ENEL.;
- O aterramento do sistema de geração deverá ser conectado ao sistema de aterramento da unidade consumidora;
- Os inversores deverão estar instalados em locais de fácil acesso, protegidos contra intempéries de acordo com o seu grau de proteção (IP), que permitam facilmente a verificação de suas características técnicas durante o processo de fiscalização/conexão da G.D;
- As instalações elétricas nestes locais deverão estar em conformidade com a NR-10, Normas técnicas/segurança da ENEL e ABNT;
- O projeto deverá atender todas as exigências da Especificação Técnica 122 - ENEL..

LEGENDA E ESPECIFICAÇÃO DOS EQUIPAMENTOS

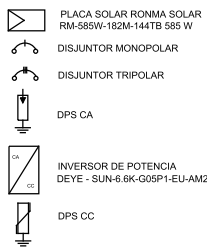

RESERVADO A Enel-RJ:

QUADRO DE REVISÕES:

REVISÃO Nº	DESCRIÇÃO	DATA
00	EMIÇÃO AUTOMÁTICA	
01	REVISAO 1	XXXX/XXXX

PROJETO DE GERAÇÃO DISTRIBUÍDA (GD)
(MICROGERAÇÃO - POTÊNCIA MENOR OU IGUAL A 10kW)

CIDADE DA OBRA:	CEP	SETOR DA OBRA:	FOTOVOLTAICA
ENDEREÇO DA OBRA:	Rua TRÊS O UNI 80 PINDOBAS MARICA RJ, CEP 24910-750		
POTÊNCIA:	1,19 kWp	UNIDADE CONSUMIDORA:	40035995
ASSINATURAS:			
PROPRIETÁRIO: MATEUS LIMA SOARES CNPJ(CPF): AUTOR DO PROJETO: CNPJ(CPF):			
ESPAÇO RESERVADO AO LOGO DA EMPRESA (SE HOUVER)	CONTEÚDO: 01-DIAGRAMA UNIFILAR; 02-DETALHES/NOTAS; 03-SITUAÇÃO.	FRANCA	
(LOGO)	DESENHO: DIAGRAMA, MATEUS, LIMA, SOARES	01/01	
	ESCALA: INDICADA		
ESTE PROJETO ESTÁ PROTEGIDO POR LEI DE DIREITO AUTURAL, SENDO PROIBIDA SUA REPRODUÇÃO TOTAL OU PARCIAL, SOB AS PENAS DA LEI 9.610 DE FEV/98			

SITUAÇÃO DA UNIDADE CONSUMIDORA
(UTILIZAR VISUALIZAÇÃO VIA
MAPA OU SATELITE)

